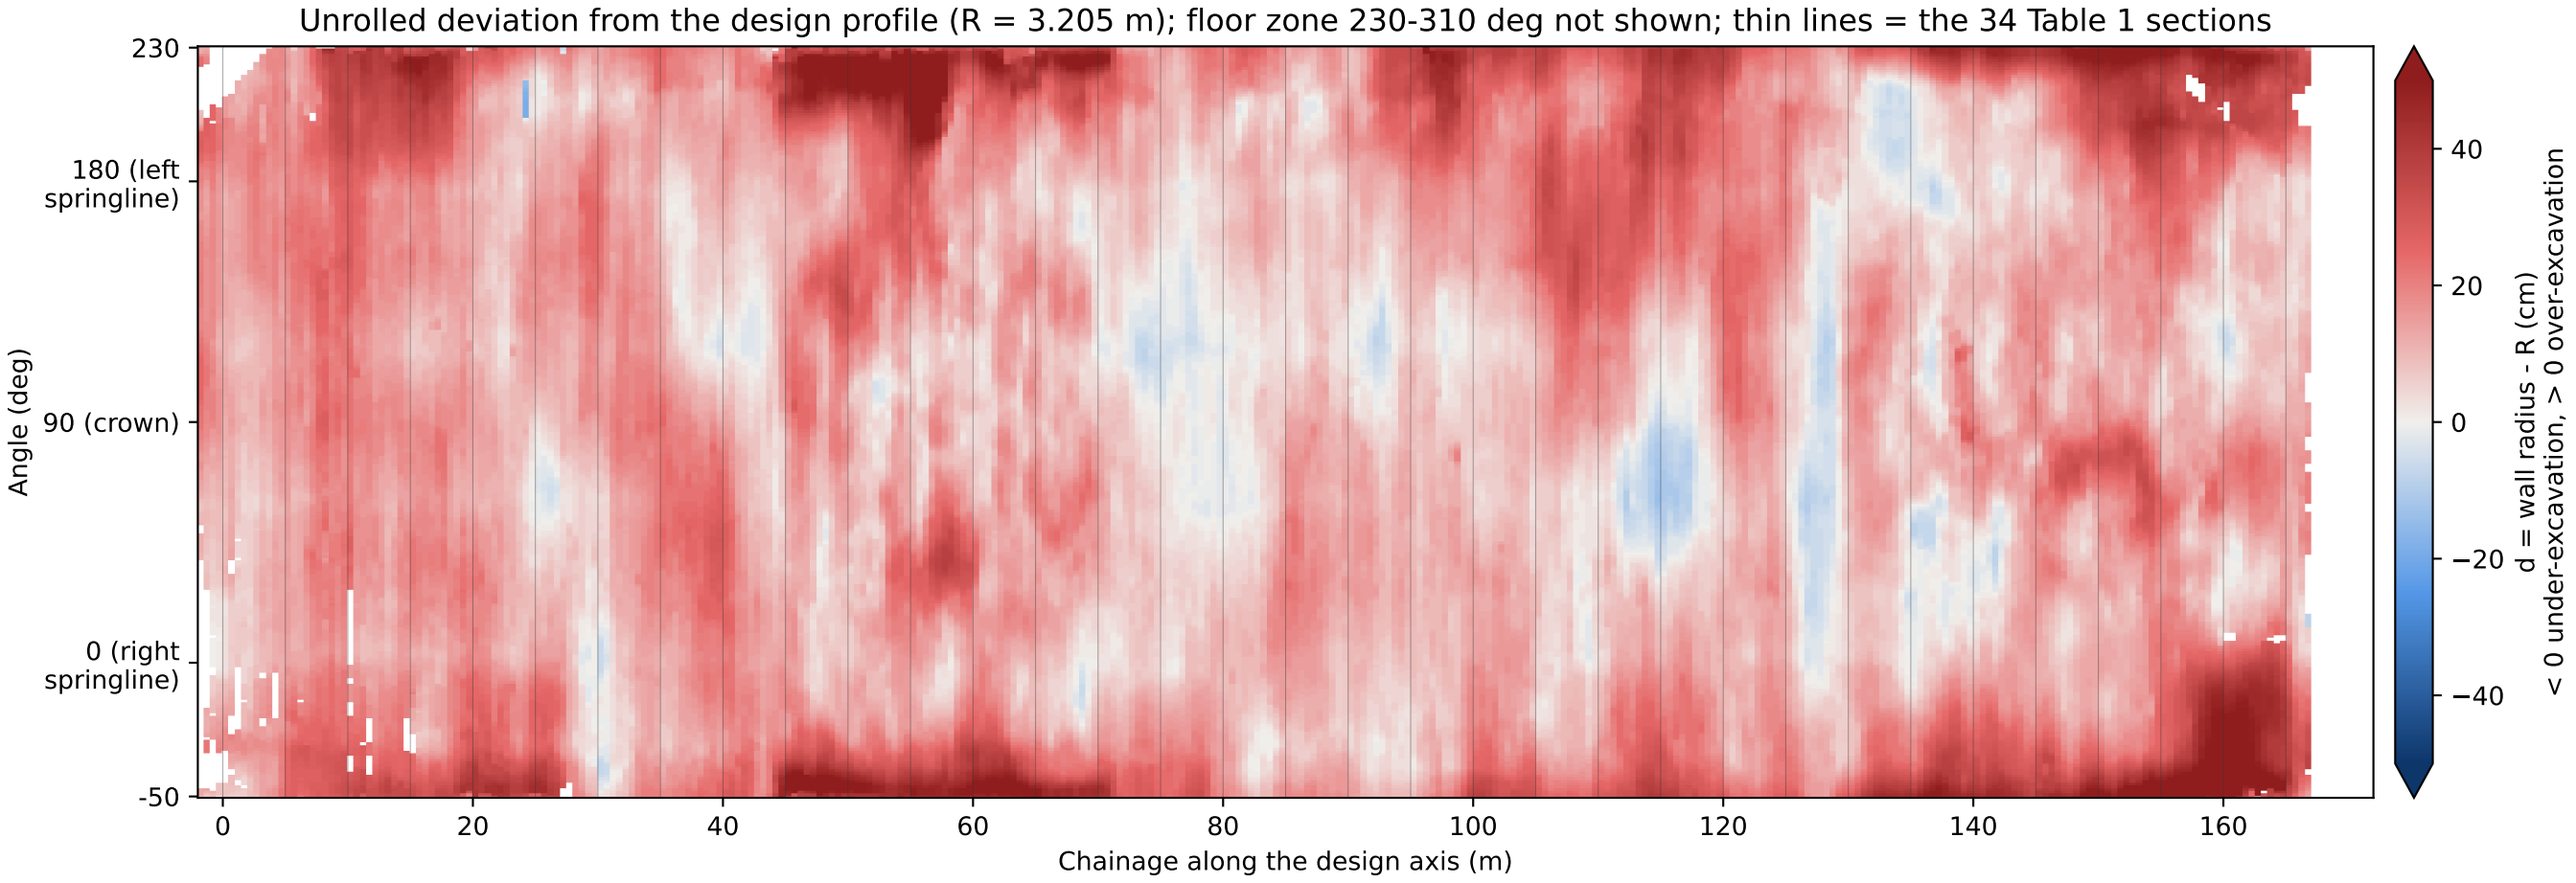

Unrolled deviation from the design profile (R = 3.205 m); floor zone 230-310 deg not shown; thin lines = the 34 Table 1 sections
230
180 (left springline)
90 (crown)
0 (right springline)
-50
Angle (deg)
0
20
40
60
80
100
120
140
160
Chainage along the design axis (m)
40
20
0
−20
−40
d = wall radius - R (cm)
< 0 under-excavation, > 0 over-excavation